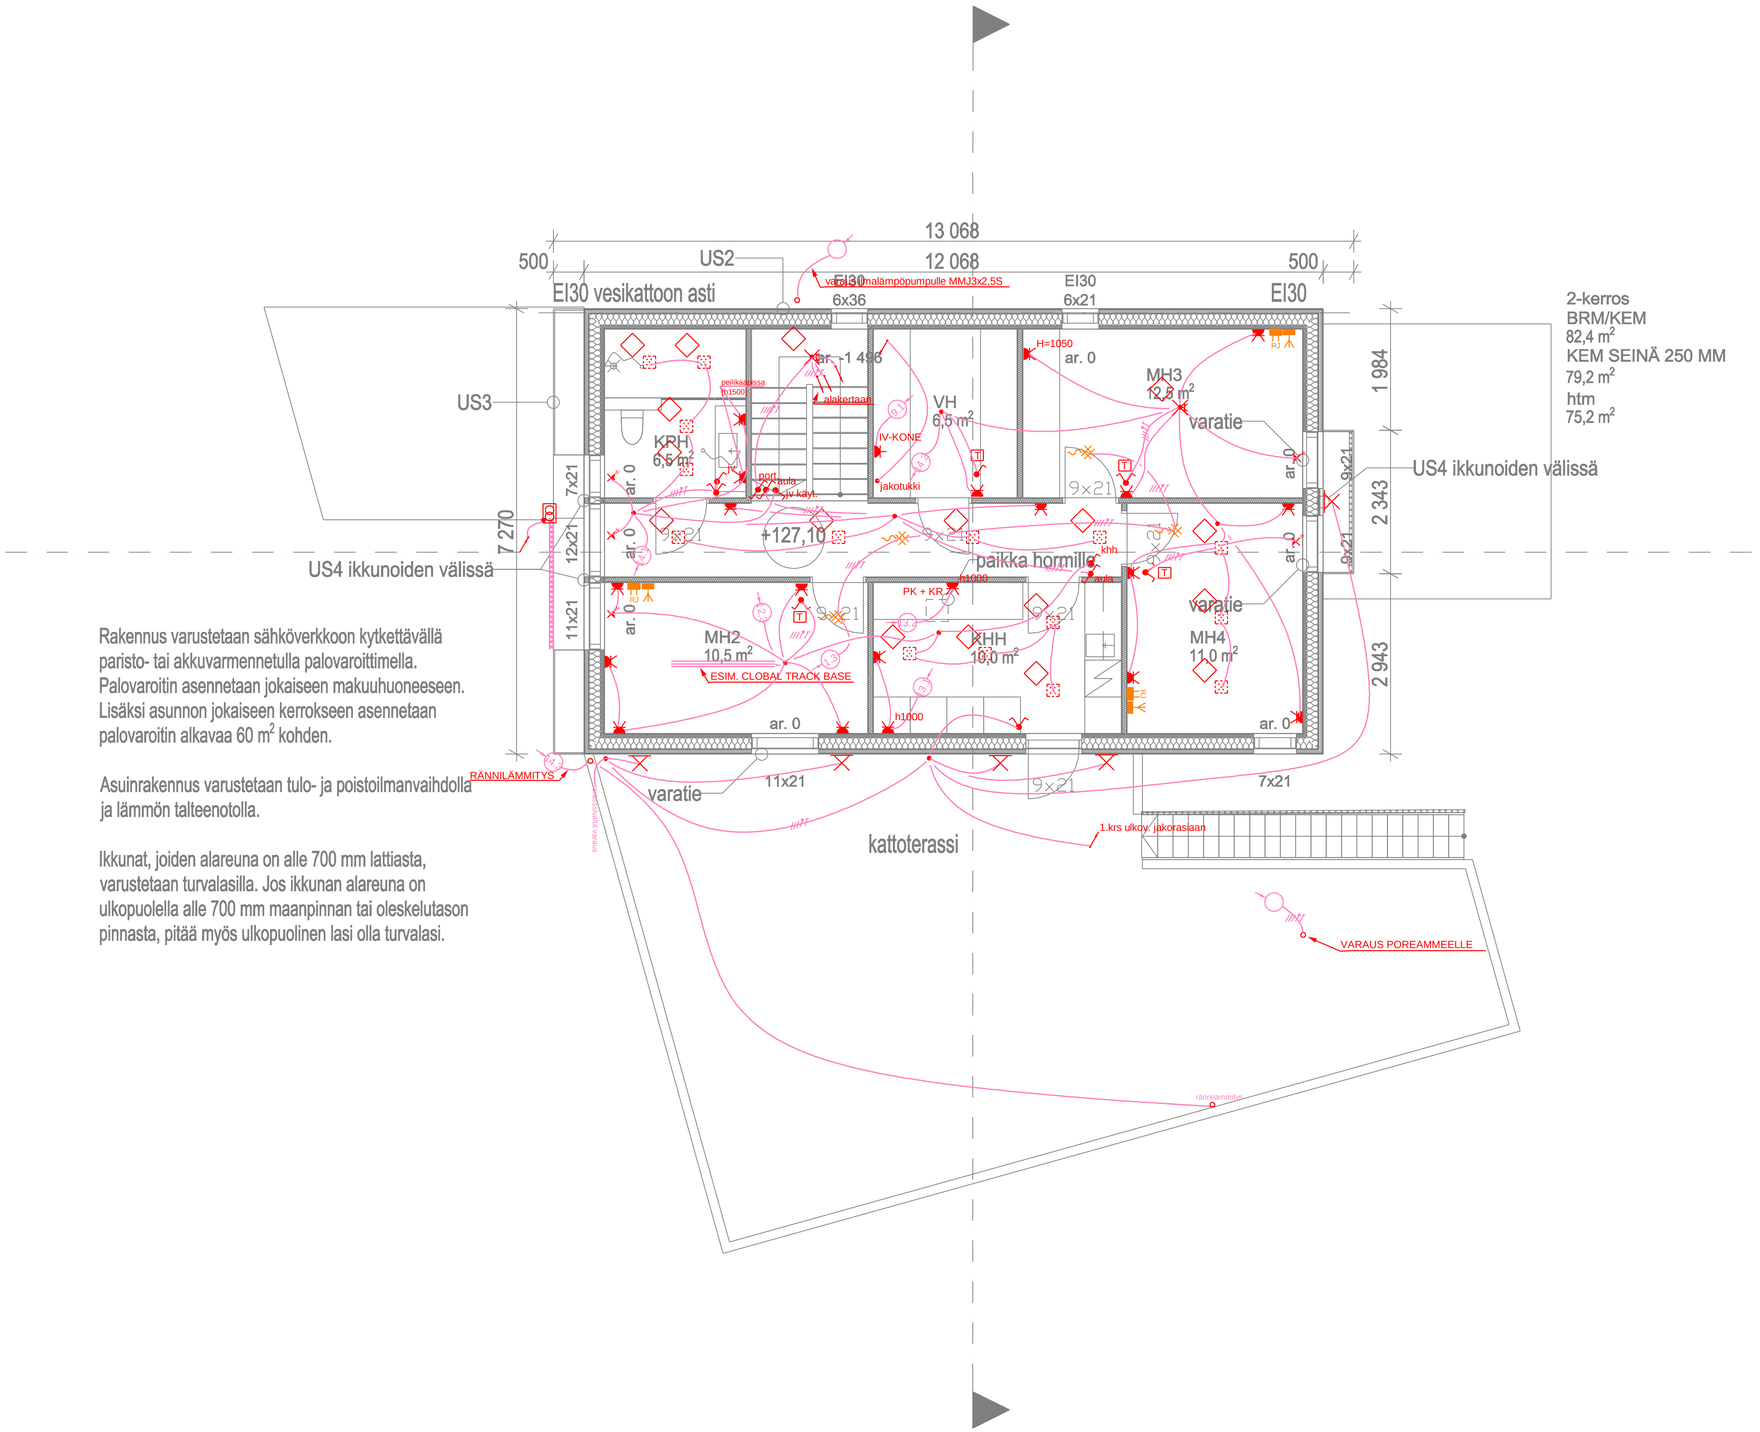

Rakennus varustetaan sähköverkkoon kytkettävällä paristo- tai akkuvarmennetulla palovaroittimella. Palovaroitin asennetaan jokaiseen makuuhuoneeseen. Lisäksi asunnon jokaiseen kerrokseen asennetaan palovaroitin alkavaa 60 m² kohden.

Asuinrakennus varustetaan tulo- ja poistoilmanvaihdolla ja lämmön talteenotolla.

Ikkunat, joiden alareuna on alle 700 mm lattiasta, varustetaan turvalasilla. Jos ikkunan alareuna on ulkopuolella alle 700 mm maanpinnan tai oleskelutason pinnasta, pitää myös ulkopuolinen lasi olla turvalasi.

K.osa/Kylä / Korttel/Tila / Tontti/Nro		Viranomaisten merkintöjä varten	
Toimenpide: Uudisrakennus		Piirustuslaji: Asennuspiirustus (työmaa)	Juoks. nro
Rakennuskohde: OKT ASIKAINEN		Piirustuksen sisältö: SÄHKÖTASO 2.KRS	Mittakaava: 1/50
KOILLIS SÄHKÖ 0400 214 150 • www.koillissahko.fi		Päiväys: 27.3.2020	Koodi / Muutos
		Työnumero: OKT ASIKAINEN	Piirustus nro: SÄH LUONNOS