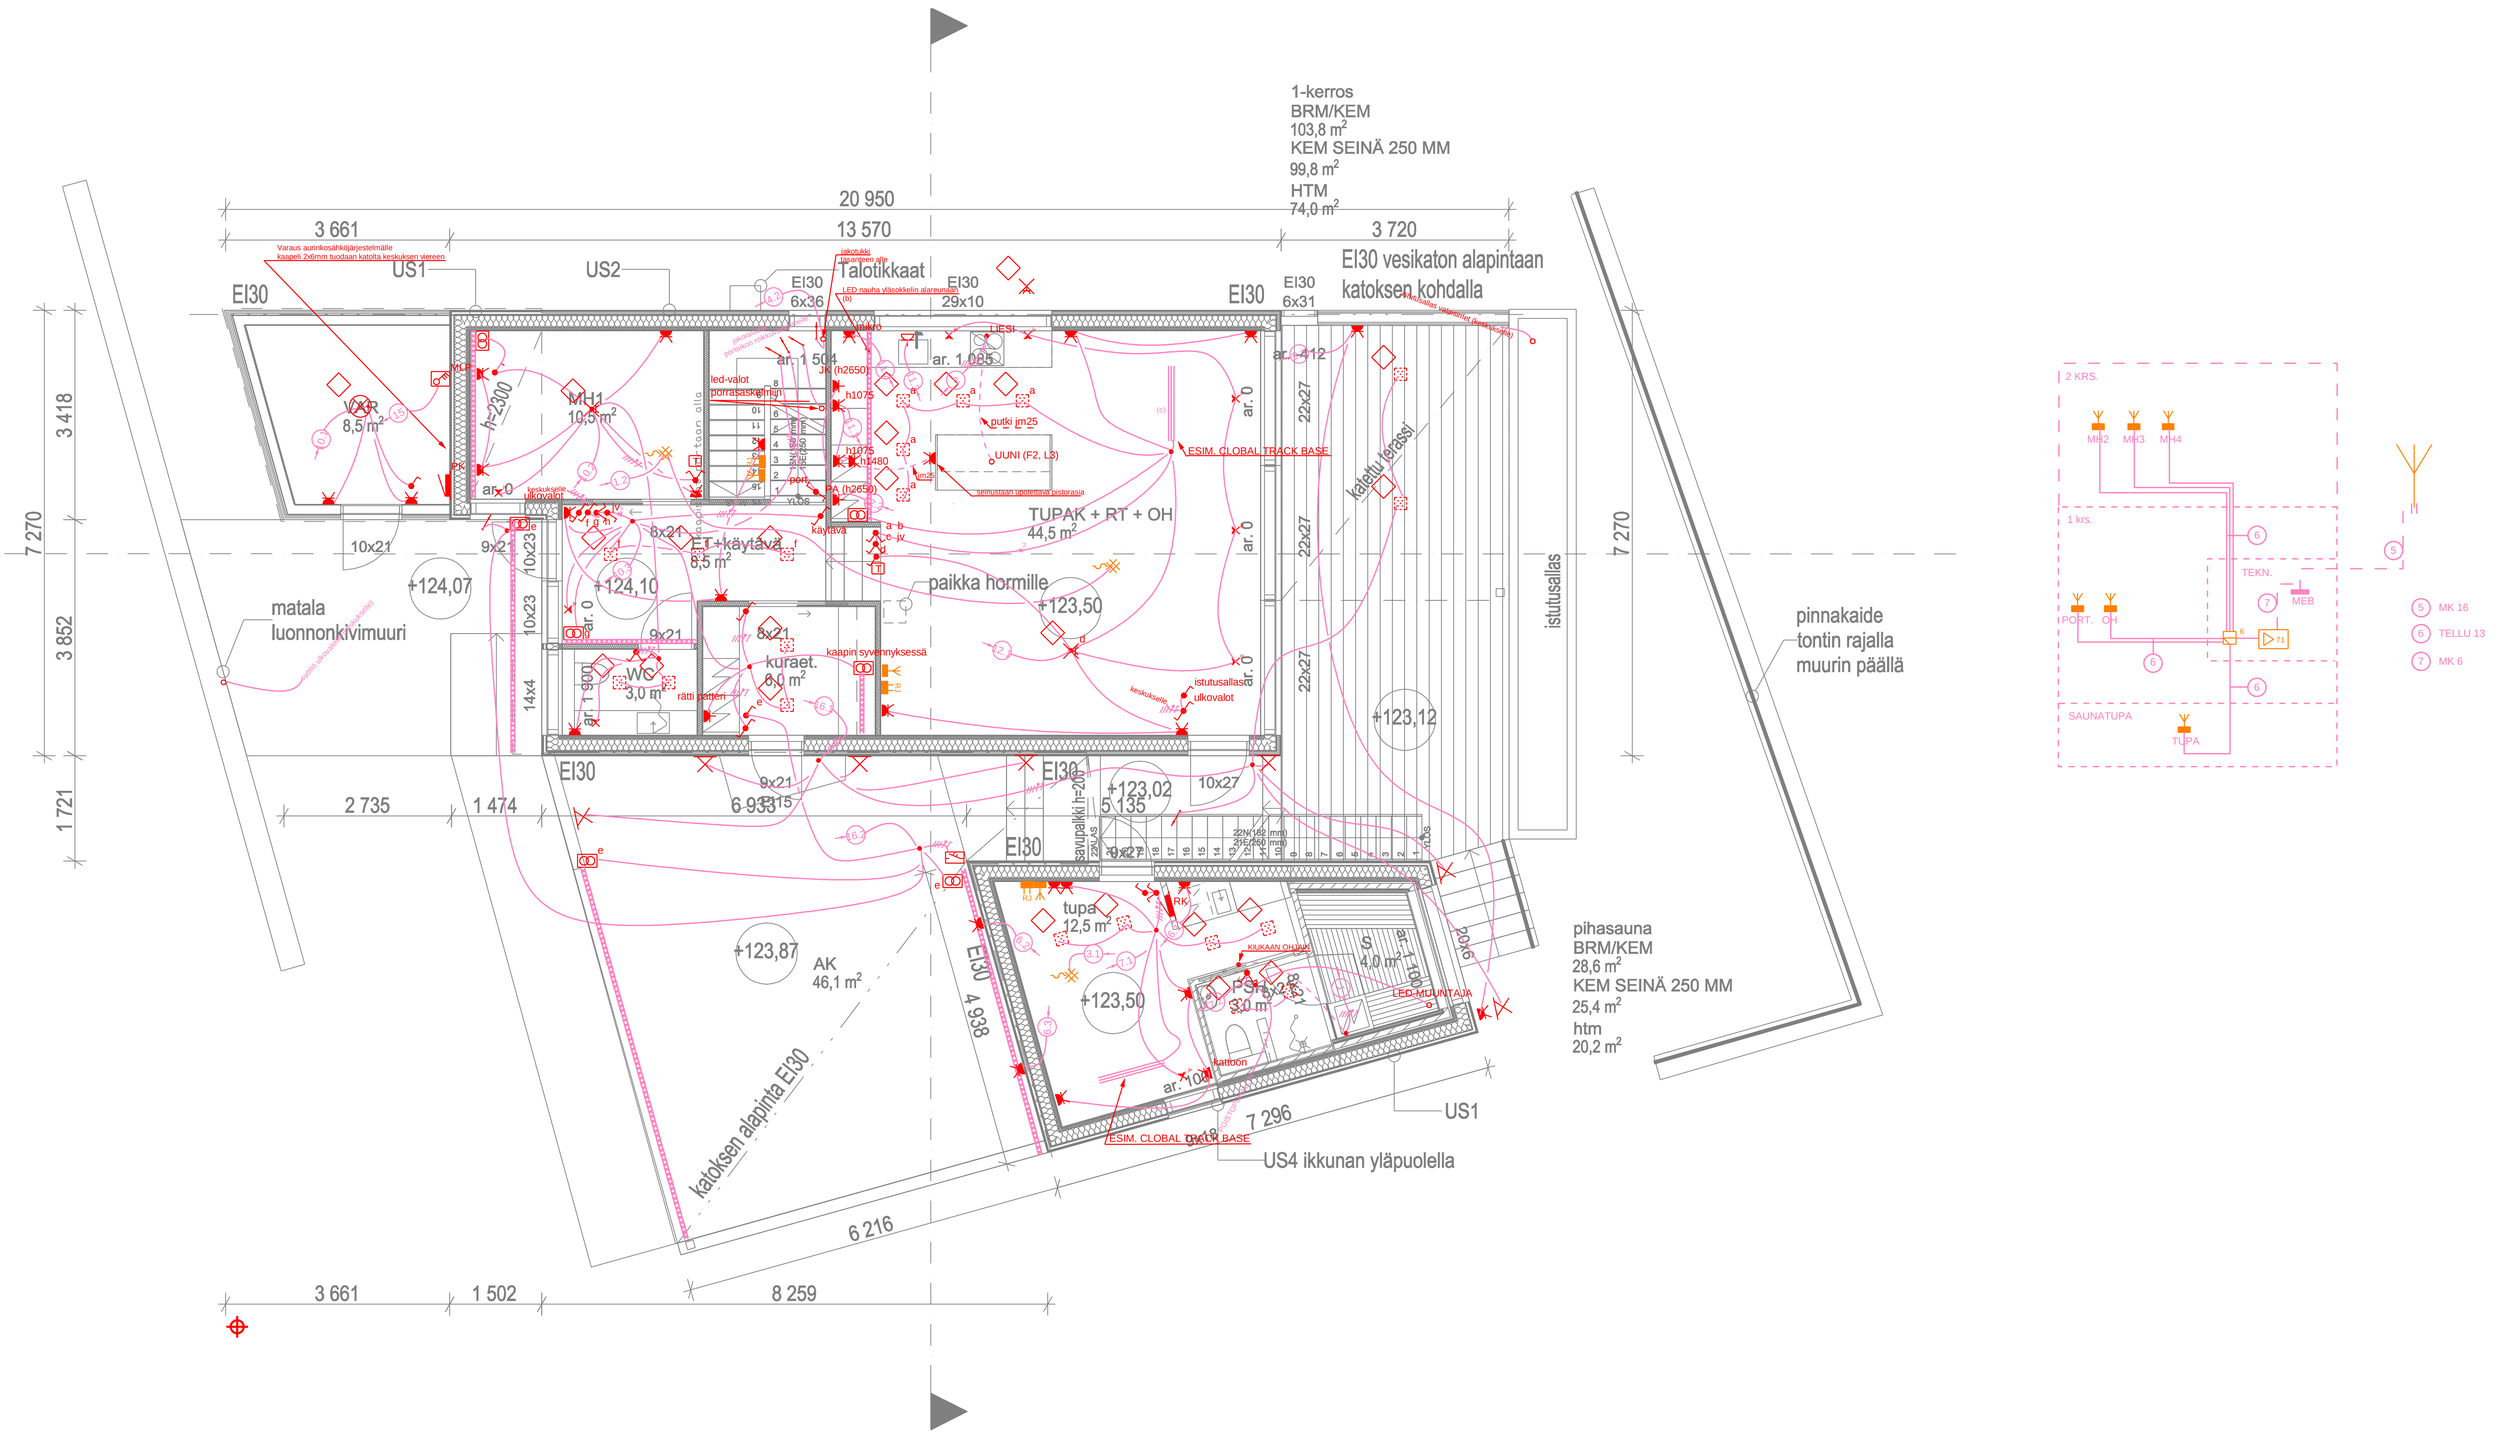

K.osa/Kylä	Korttel/Tila	Tontti/Nro	Viranomaisten merkintöjä varten		
Toimenpide: Uudisrakennus			Piirustuslaji: Asennuspiirustus (työmaa)		Juoks. nro
Rakennuskohde: OKT ASIKAINEN			Piirustuksen sisältö: SÄHKÖTASO 1.KRS		Mittakaava: 1/50
KOILLIS SÄHKÖ 0400 214 150 • www.koillissahko.fi			Päiväys: 27.3.2020	Koodi	Muutos
			Työnumero: OKT ASIKAINEN	Piirustus nro: SÄH LUONNOS	