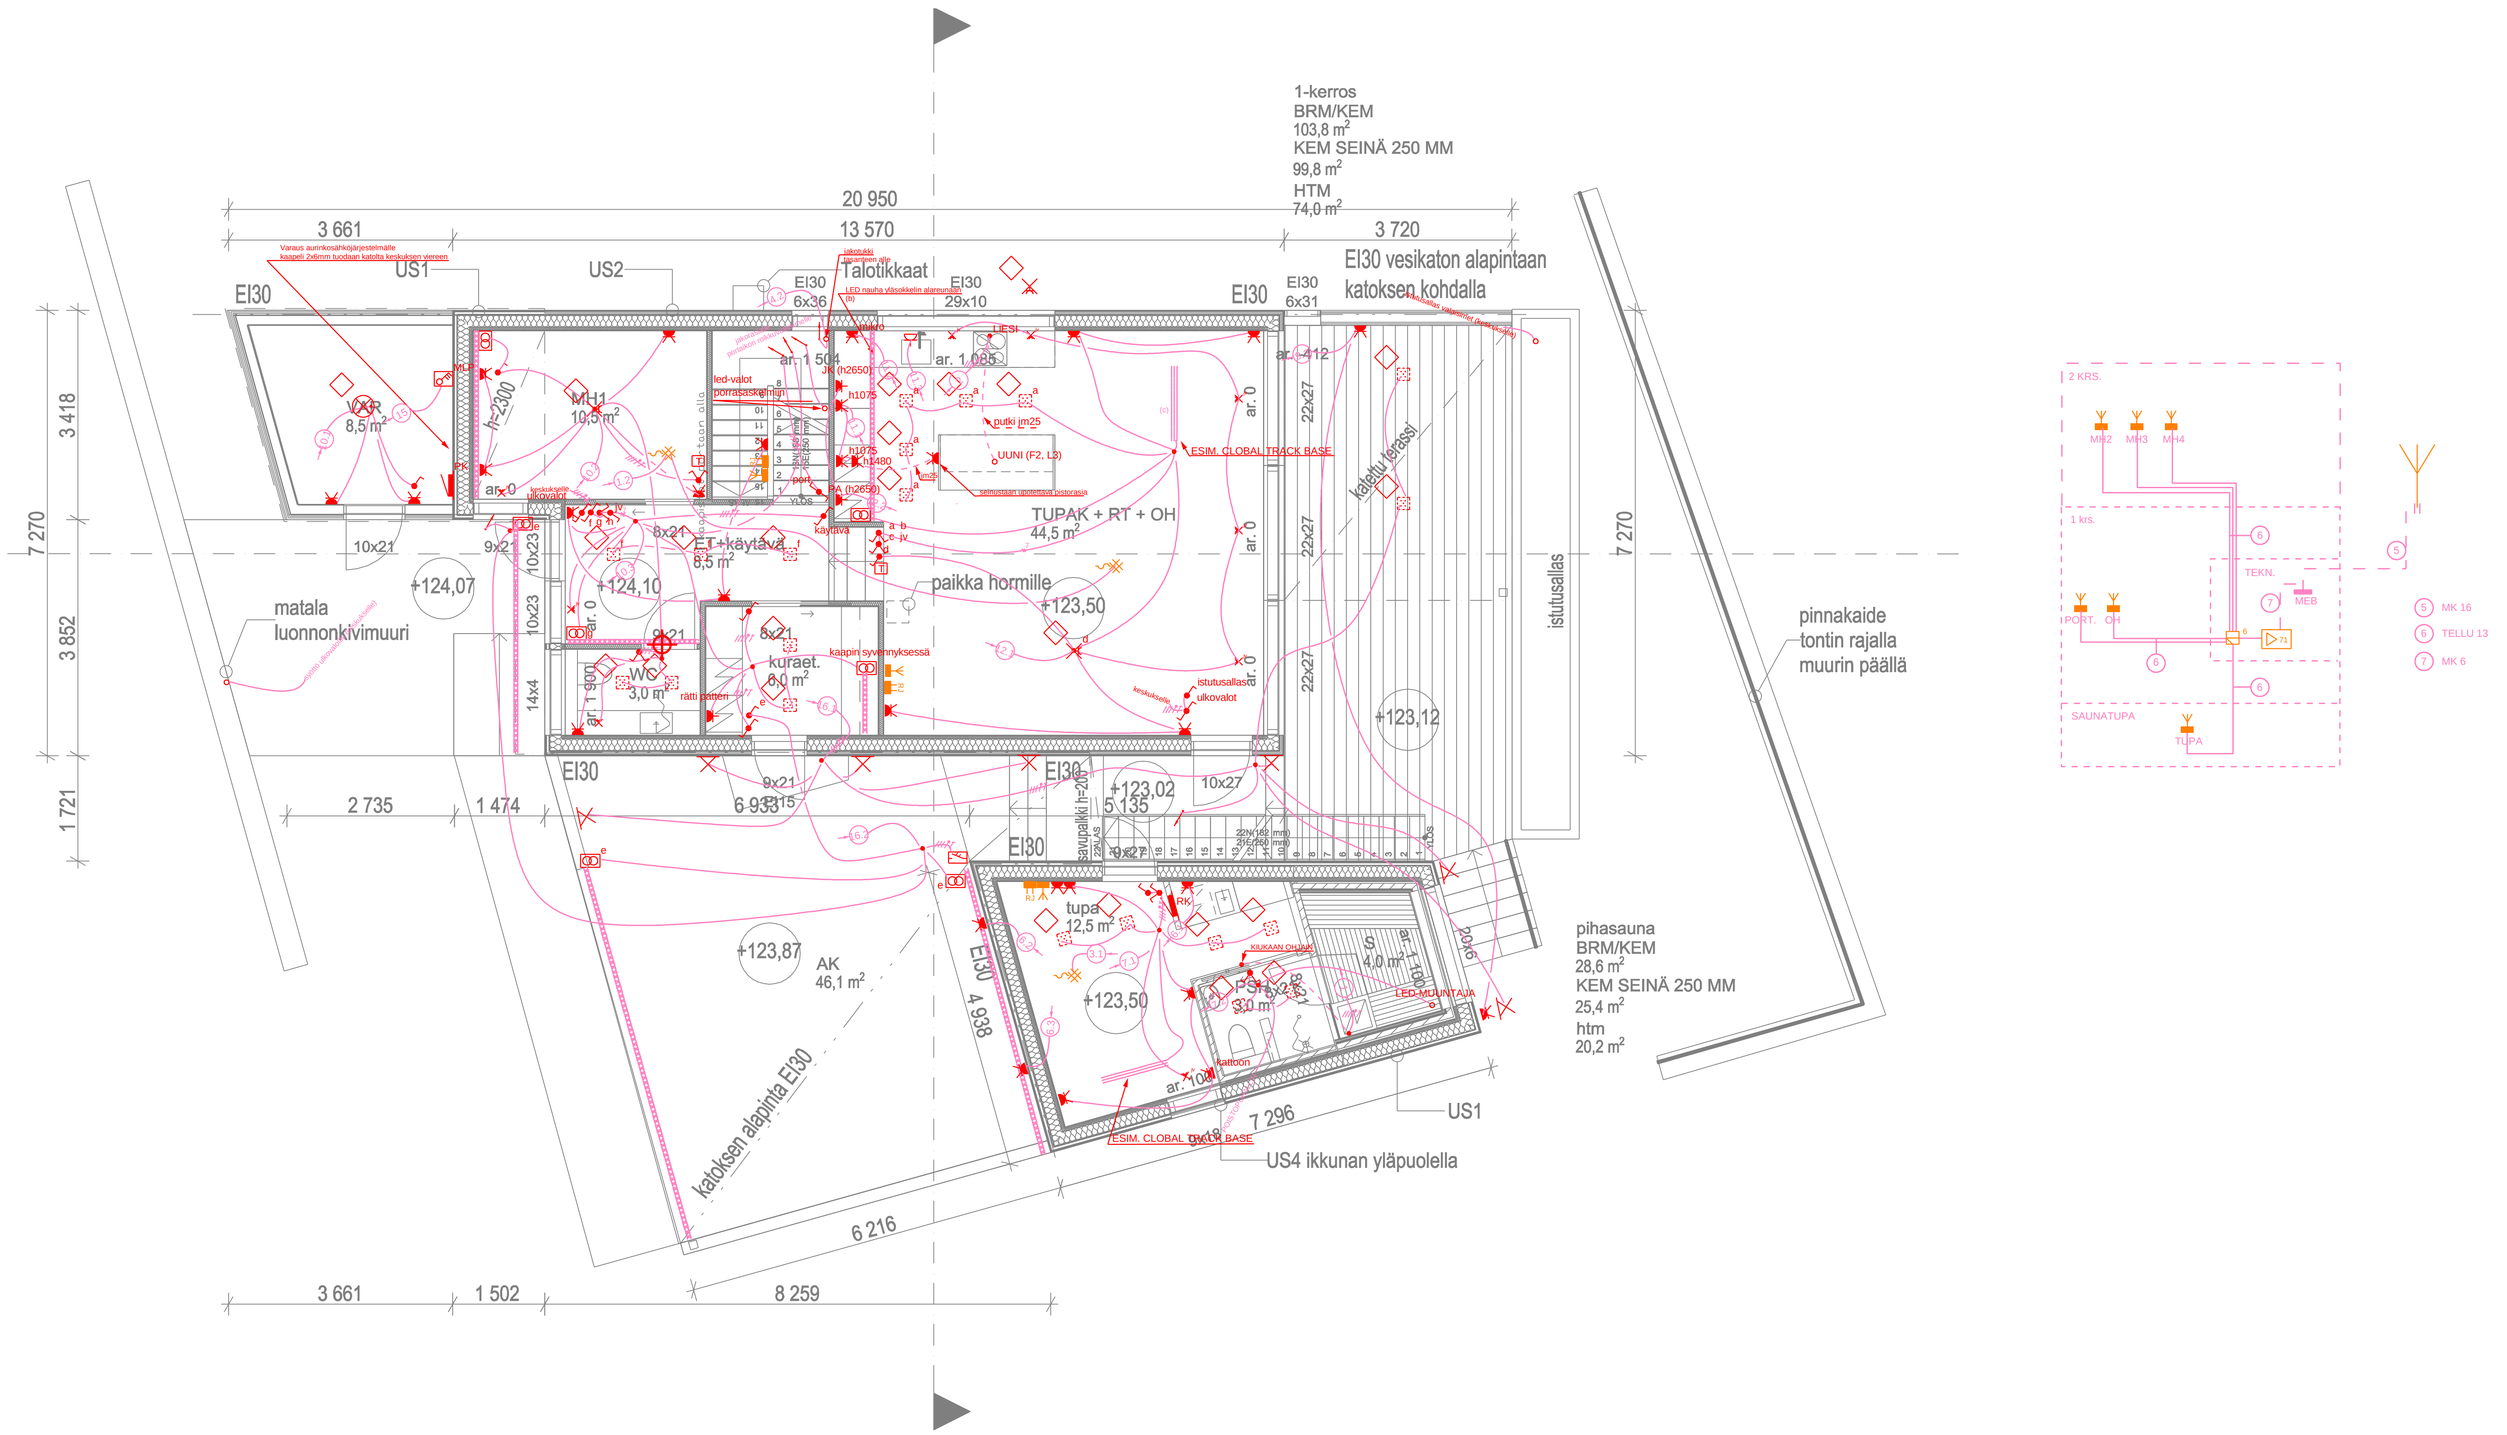


| | | | |
|---|---|---|---|
| K.osa/Kylä / Korttel/Tila / Tontti/Nro | Viranomaisten merkintöjä varten | | |
| Toimenpide: Uudisrakennus | Piirustuslaji: Asennuspiirustus (työmaa) | | Juoks. nro |
| Rakennuskohde: OKT ASIKAINEN | Piirustuksen sisältö: SÄHKÖTASO 1.KRS | | Mittakaava: 1/50 |
| KOILLIS SÄHKÖ 0400 214 150 • www.koillissahko.fi | Päiväys: 27.3.2020 | Koodi | Muutos |
| | Työnumero: OKT ASIKAINEN | Piirustus nro: SÄH LUONNOS | |