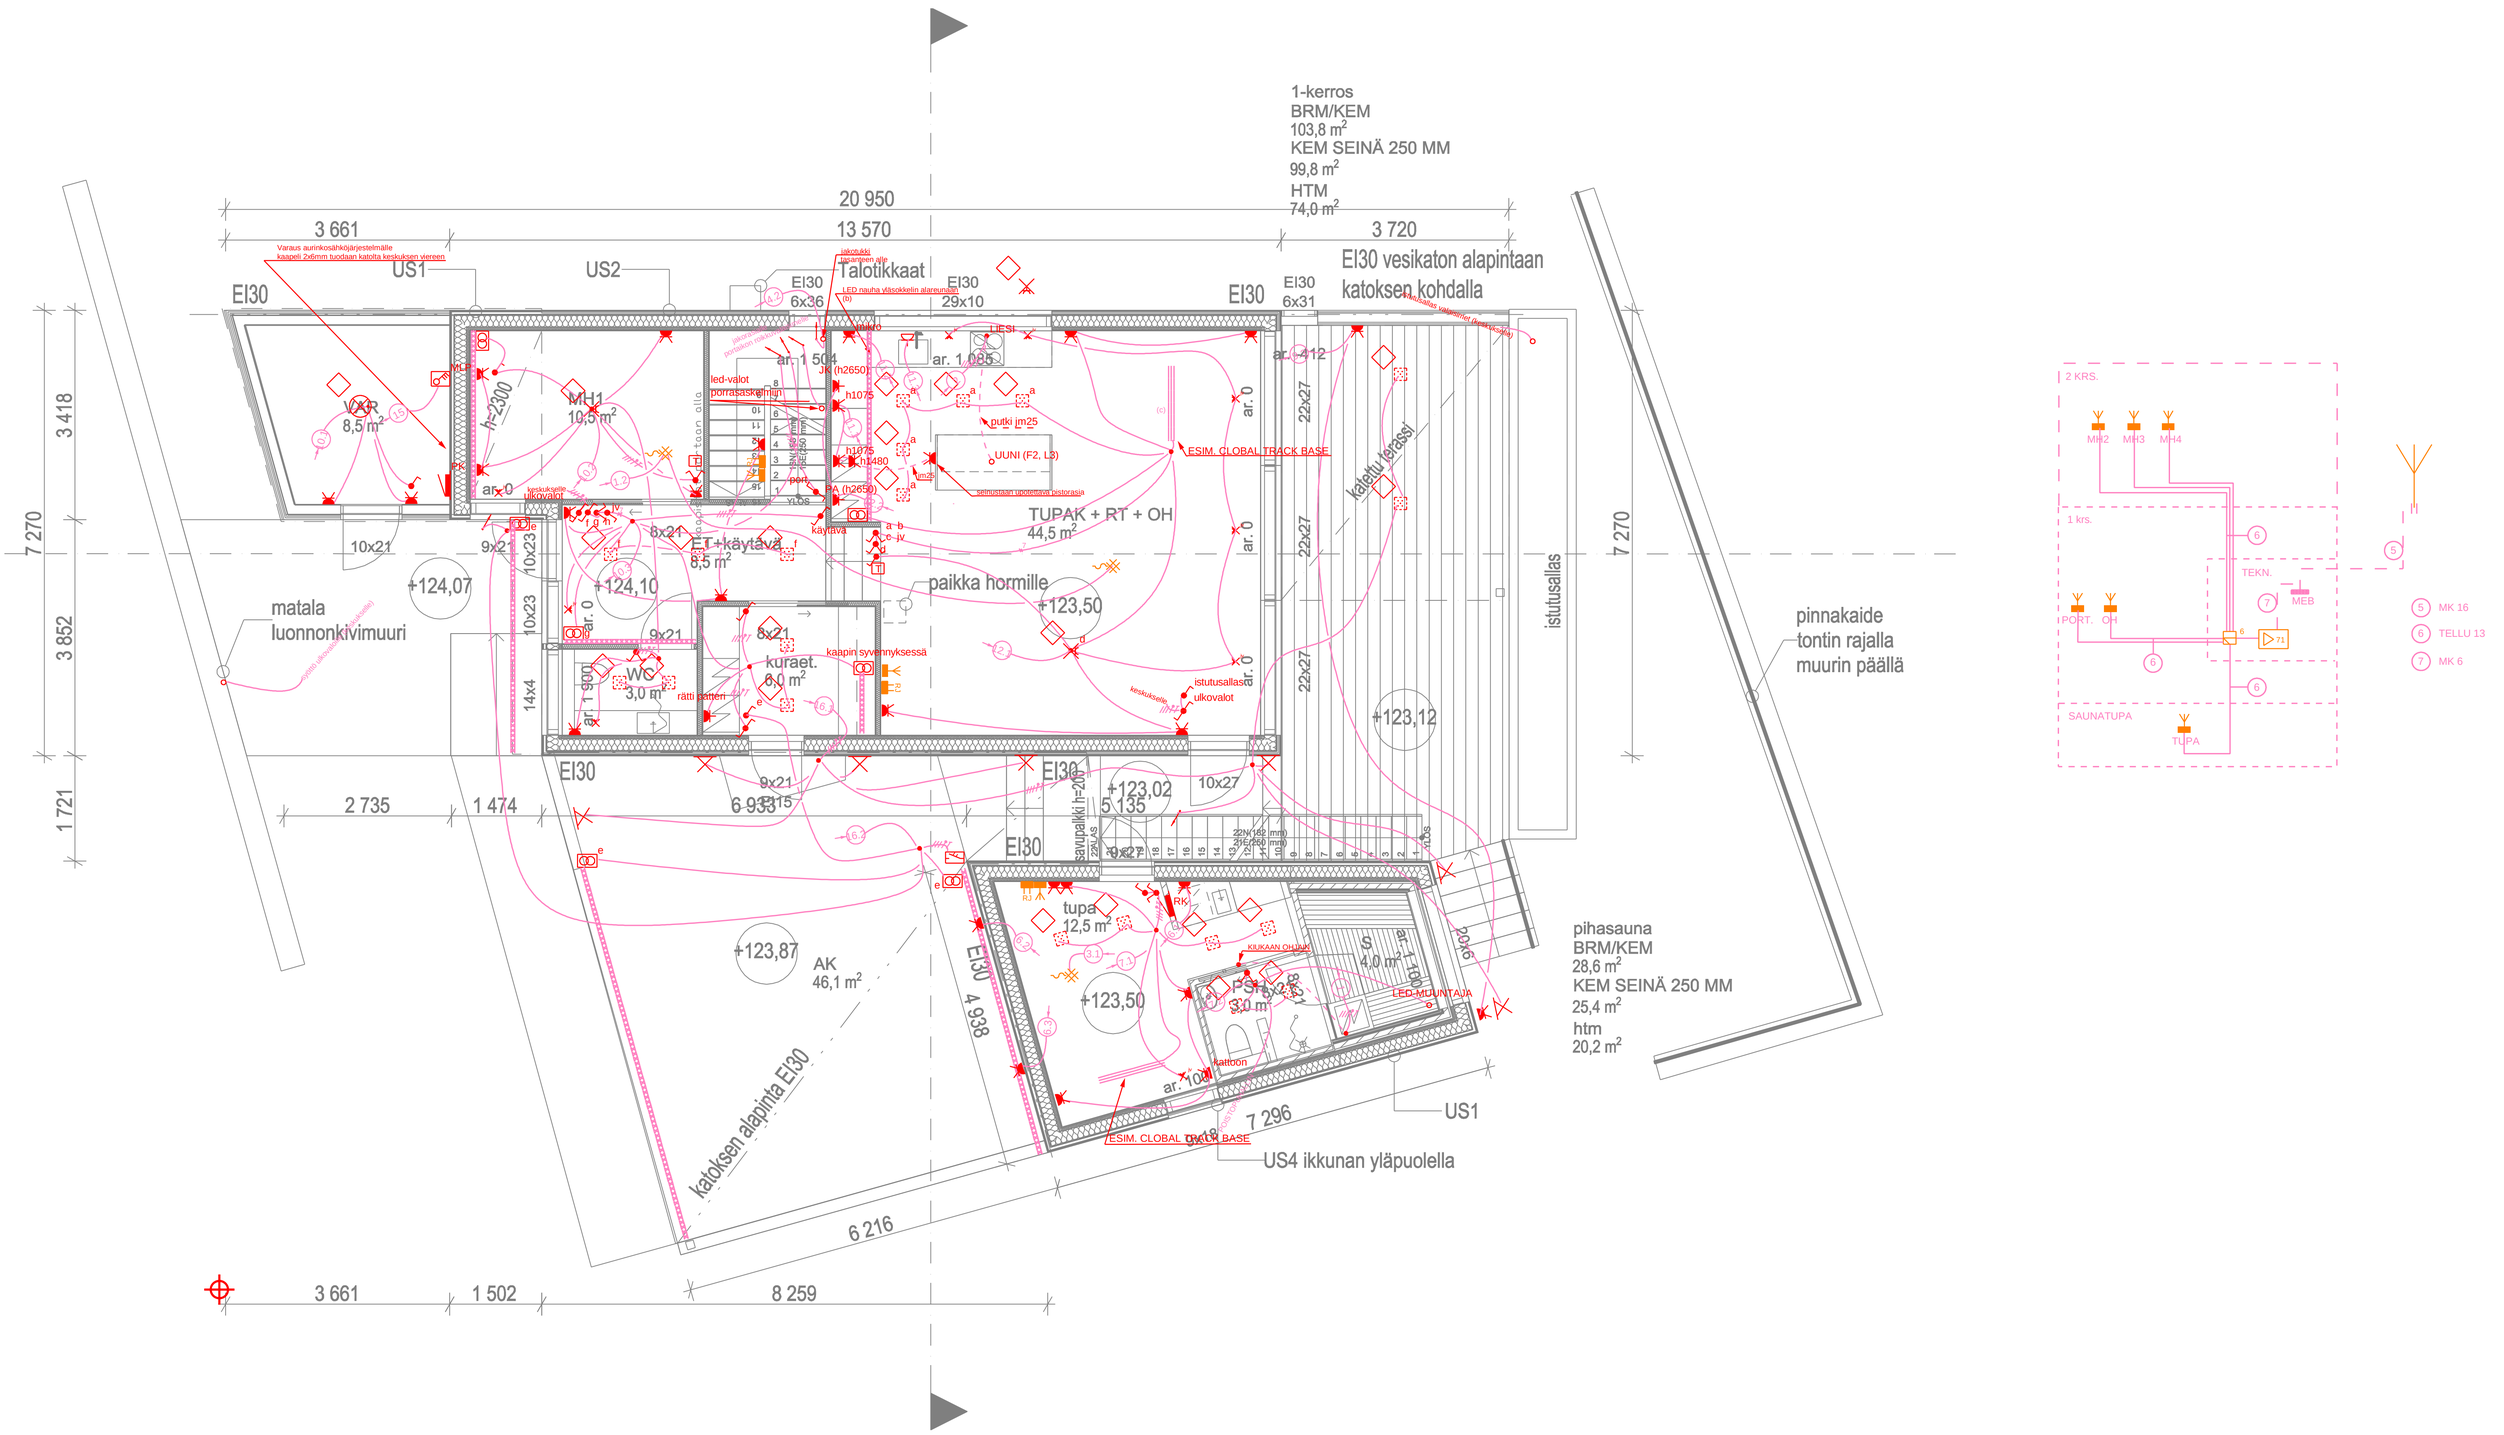

K.osa/Kylä / Korttel/Tila / Tontti/Nro	Viranomaisten merkintöjä varten		
Toimenpide: Uudisrakennus	Piirustuslaji: Asennuspiirustus (työmaa)		Juoks. nro
Rakennuskohde: OKT ASIKAINEN	Piirustuksen sisältö: SÄHKÖTASO 1.KRS		Mittakaava: 1/50
KOILLIS SÄHKÖ 0400 214 150 • www.koillissahko.fi	Päiväys: 27.3.2020	Koodi	Muutos
	Työnumero: OKT ASIKAINEN	Piirustus nro: SÄH LUONNOS	